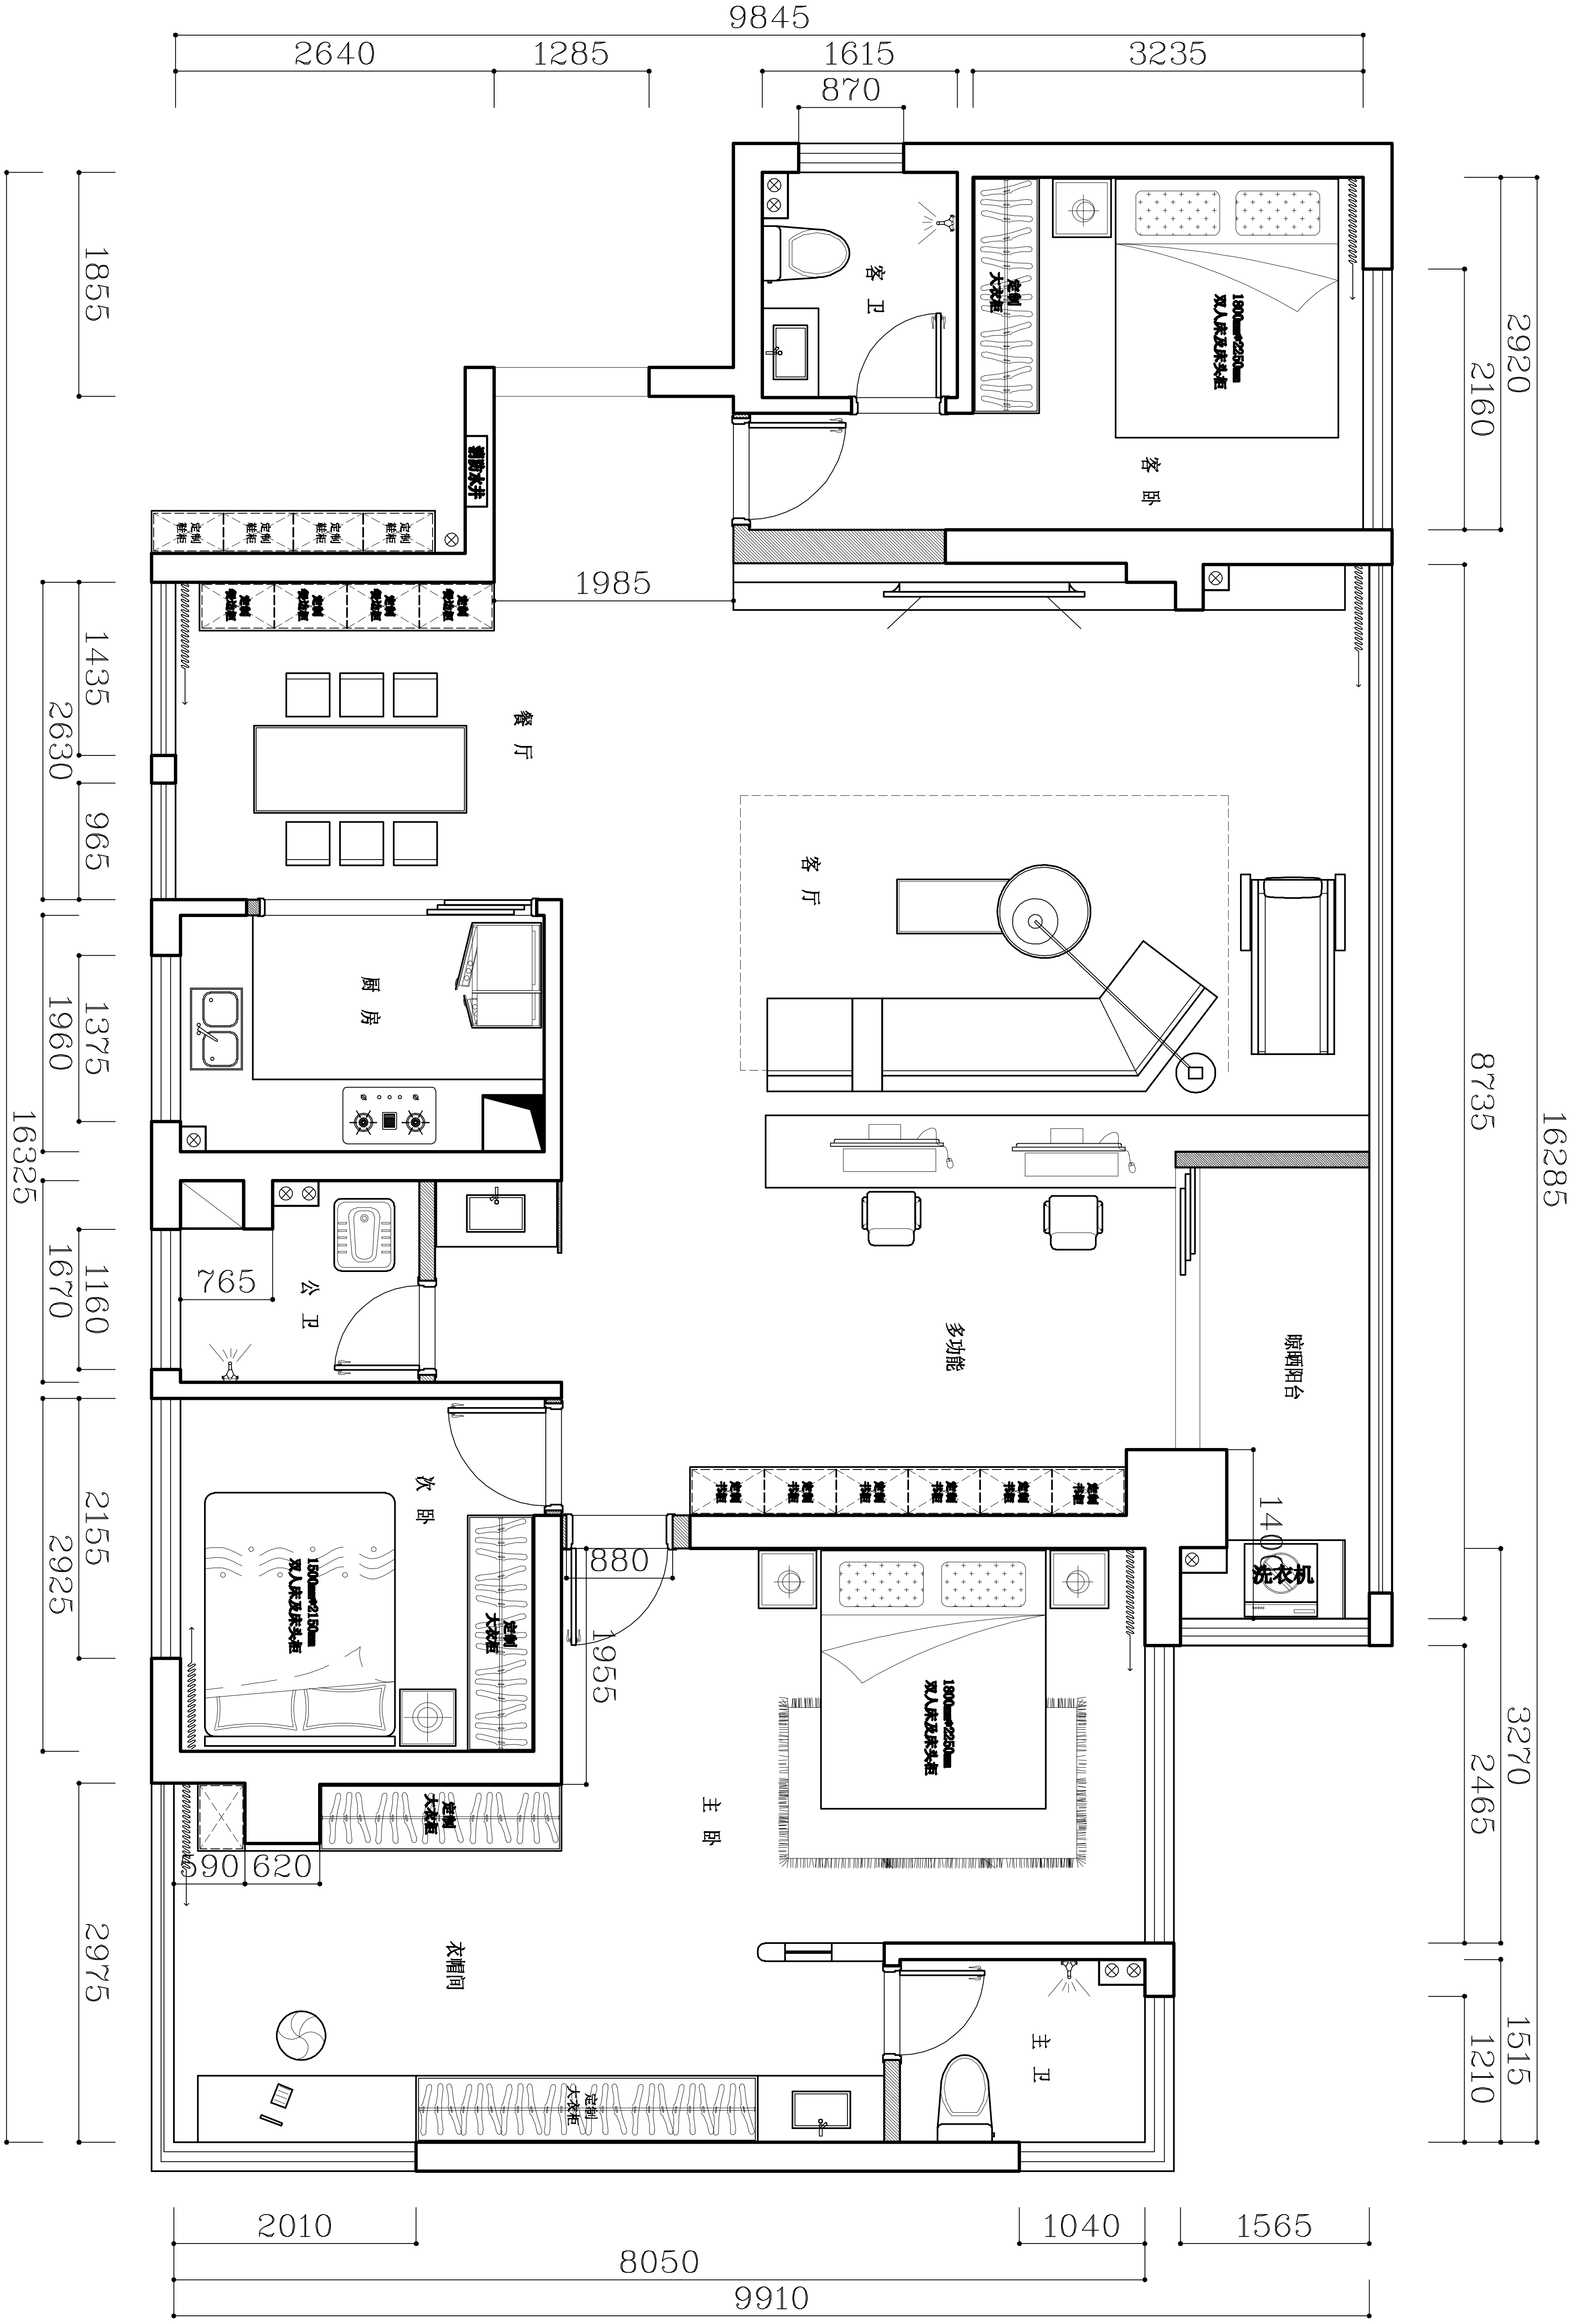
9845
2640
1285
1615
3235
870
客卫
定制大衣柜
1800mm*2250mm双人床及床头柜
客卧
消防水井
定制鞋柜
定制餐边柜
1985
餐厅
客厅
厨房
公卫
765
多功能
晾晒阳台
定制书柜
1400
洗衣机
次卧
1500mm*2150mm双人床及床头柜
定制大衣柜
880
1955
主卧
1800mm*2250mm双人床及床头柜
590
620
衣帽间
主卫
1855
1435
2630
965
1375
1960
16325
1160
1670
2155
2925
2975
2920
2160
8735
16285
3270
2465
1515
1210
2010
1040
1565
8050
9910